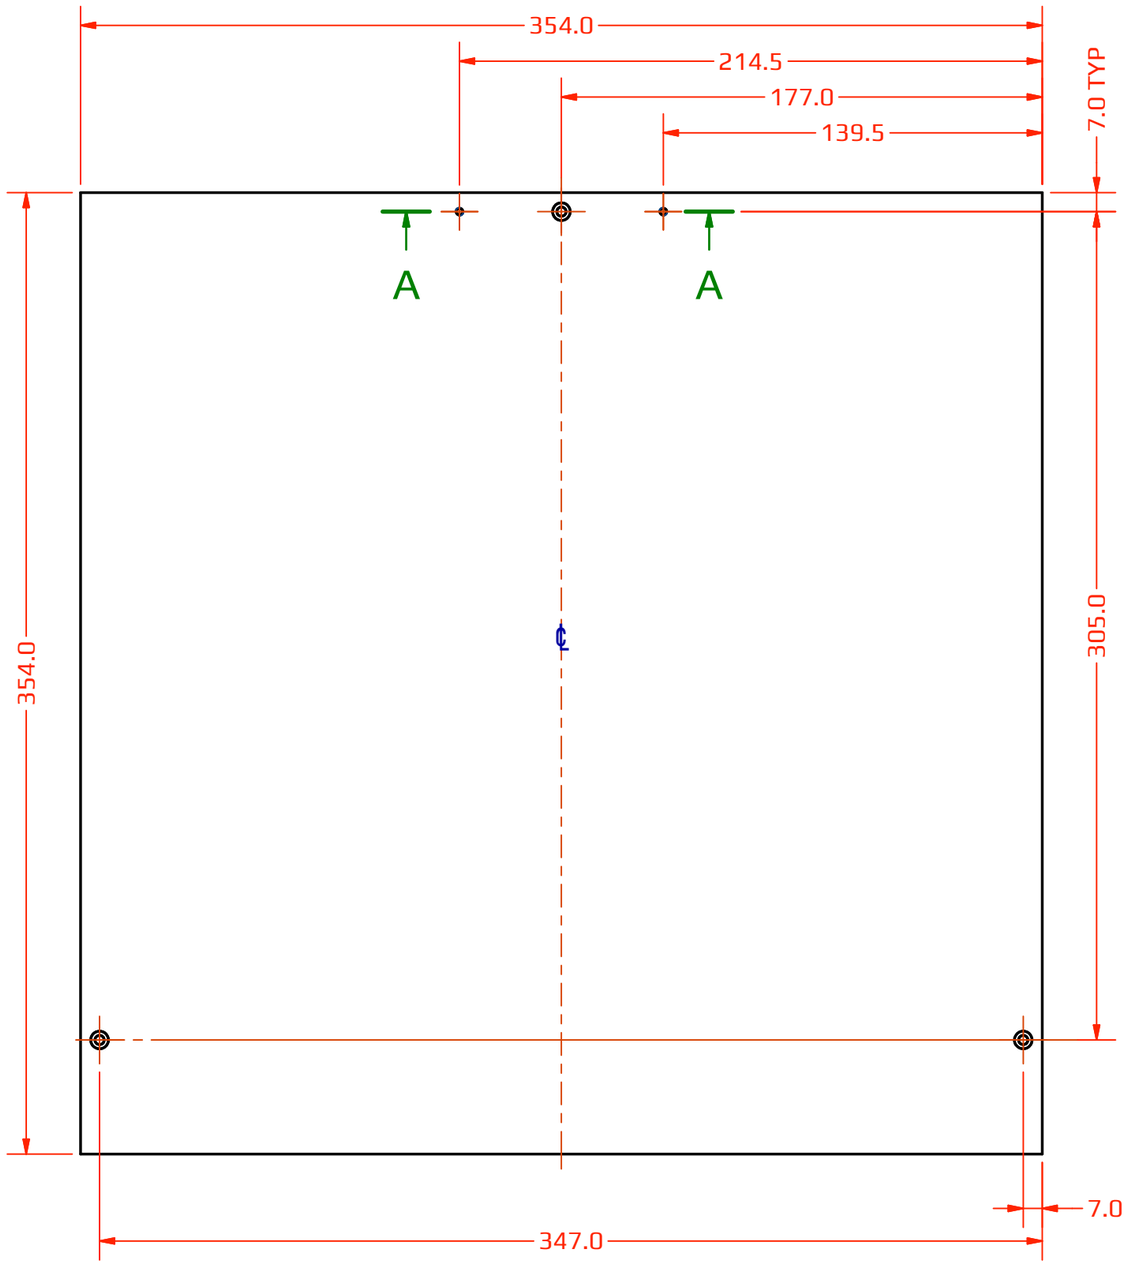


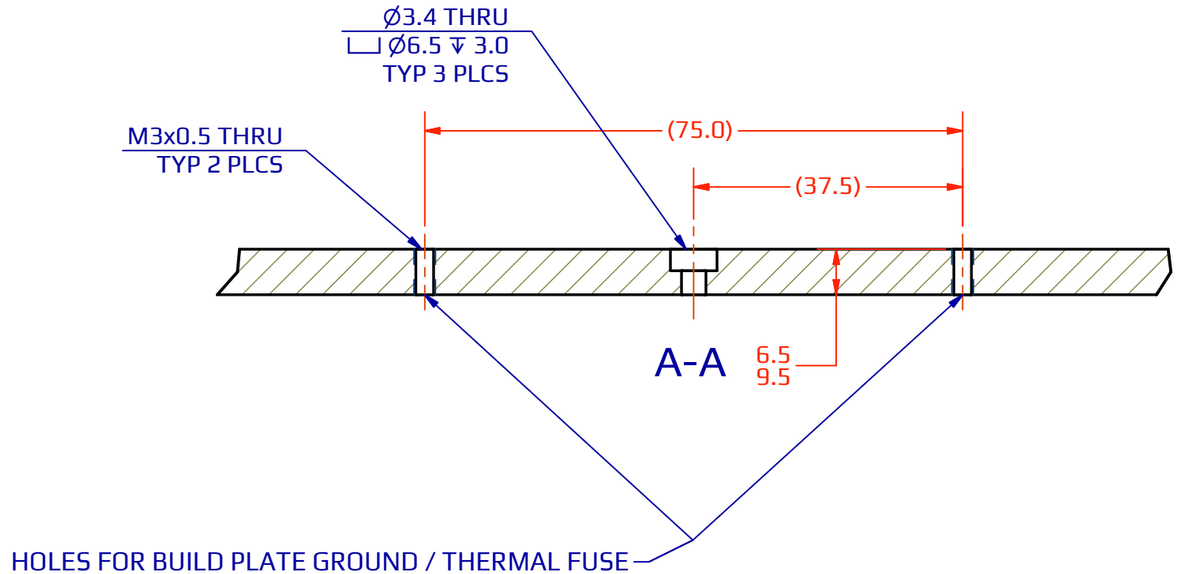


## GENERAL NOTES:

1. MATERIAL TO BE CAST ALUMINUM TOOLING PLATE (MIC-6, ATP-5, ALCA 5, OR EQUIVALENT).
2. BUILD PLATE DIMENSIONS AND HOLE SPACINGS MUST BE ADJUSTED FOR NON-STANDARD BUILD SIZES (NOMINAL PRINT SIZE FOR THE GIVEN AXIS + 4mm) AND ALL OTHER DIMENSIONS MUST BE ADJUST TO SUIT.
3. ALL DIMENSIONS IN mm.
4. TOLERANCES ARE +/- 0.5mm UNLESS OTHERWISE NOTED.
5. BREAK ALL SHARP EDGES.

VORON DESIGN

| | | | |
|---|---|---|---|
| PROJECT: VORON TRIDENT | | | |
| DRAWING TITLE: TRIDENT BUILD PLATE - 350x350 | | | |
| DWN: WILE.E | SCALE: N.T.S. | PG NO: 1 OF 1 | |
| DATE: 8/12/2021 | FILE NO: VRN-BP-VT-350 | | REV: 0 |